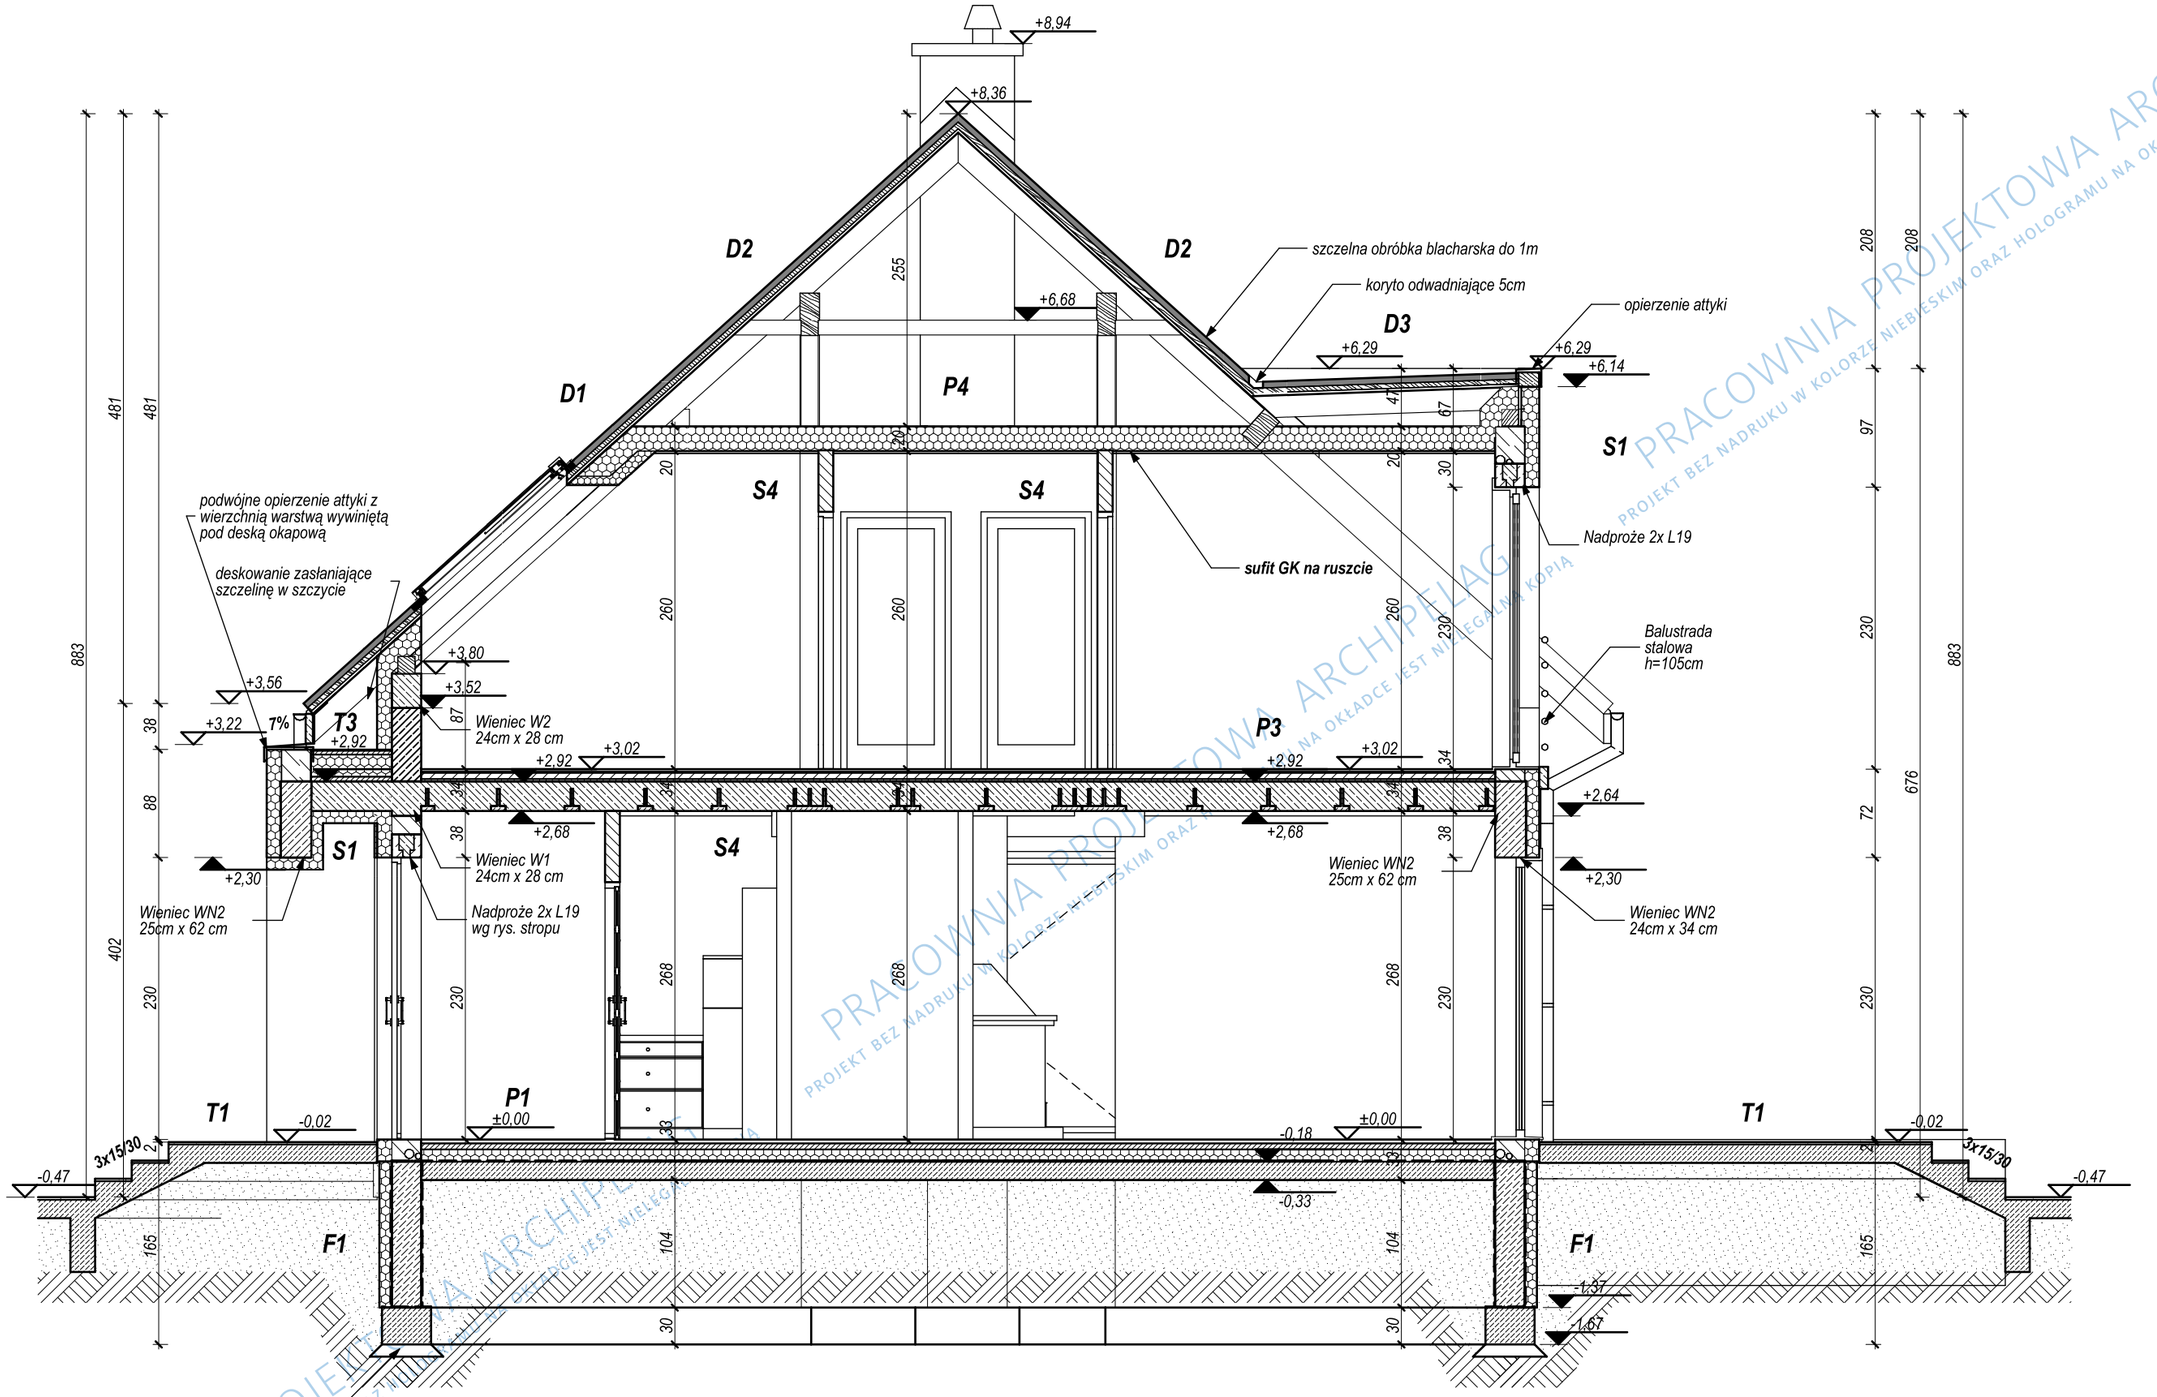

UWAGI: wylewka betonowa 10 cm

OPIS WARSTW PRZEGRÓD BUDOWLANYCH POKAZANO NA RYS. NR A9.

FUNDAMENTY WYKONAC WG RYSUNKÓW KONSTRUKCYJNYCH.

WSZYTKIE ELEMENTY DREWNIANE NA STYKU Z MUREM IZOLOWAC PRZEKLADKĄ Z PAPY.

WSZYTKIE ELEMENTY DREWNIANE PRZED WMONTOWANIEM NALEŻY ZAIMPREGNOWAĆ WG OPISU TECHNICZNEGO.

ZESTAWIENIE ELEMENTÓW DREWNIANYCH WG ZESTAWIENIA WIĘŻBY.

PRACOWNIA PROJEKTOWA ARCHIPELAG
PROJEKT BEZ NADRUKU W KOLORZE NIEBIESKIM ORAZ HOLOGRAMU NA OKŁADCE JEST NIELEGALNĄ KOPIĄ

GRUPA ARCHIPELAG | ARCHIPELAG.PL

tytuł rysunku: PRZEKRÓJ A-A	skala: 1:50	projektant projektu gotowego: Artur Wójciak	nr upr.: 394/94/UW	podpis:
obiekt: JEDNORODZINNY DOM WOLNOSTOJĄCY "MATI G1"	branża: ARCH.	Rysunek o charakterze pokazowym. Stanowi część dokumentacji technicznej projektu domu katalogowego autorstwa Pracowni Projektowej ARCHIPELAG i jest wyłączną własnością Pracowni, chronioną prawami autorskimi. Rozpowszechnianie i kopiowanie bez zgody autorów zabronione pod rygorem pełnej odpowiedzialności cywilnej i karnej.		
adres budowy:				

PRACOWNIA PROJEKTOWA ARCHIPELAG, ul. Czysta 2-4, 50-013 Wrocław, tel. 071/798 38 00, fax 071/798 38 69, biuro@archipelag.pl www.archipelag.pl

nr rys: A6 | data: